

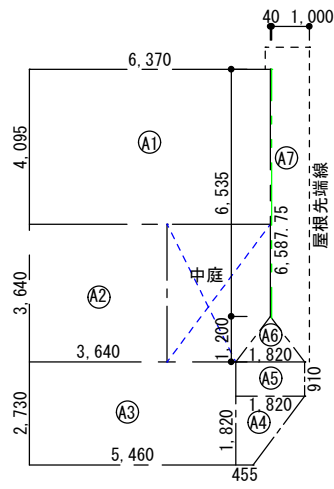
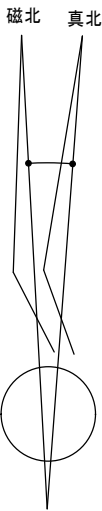


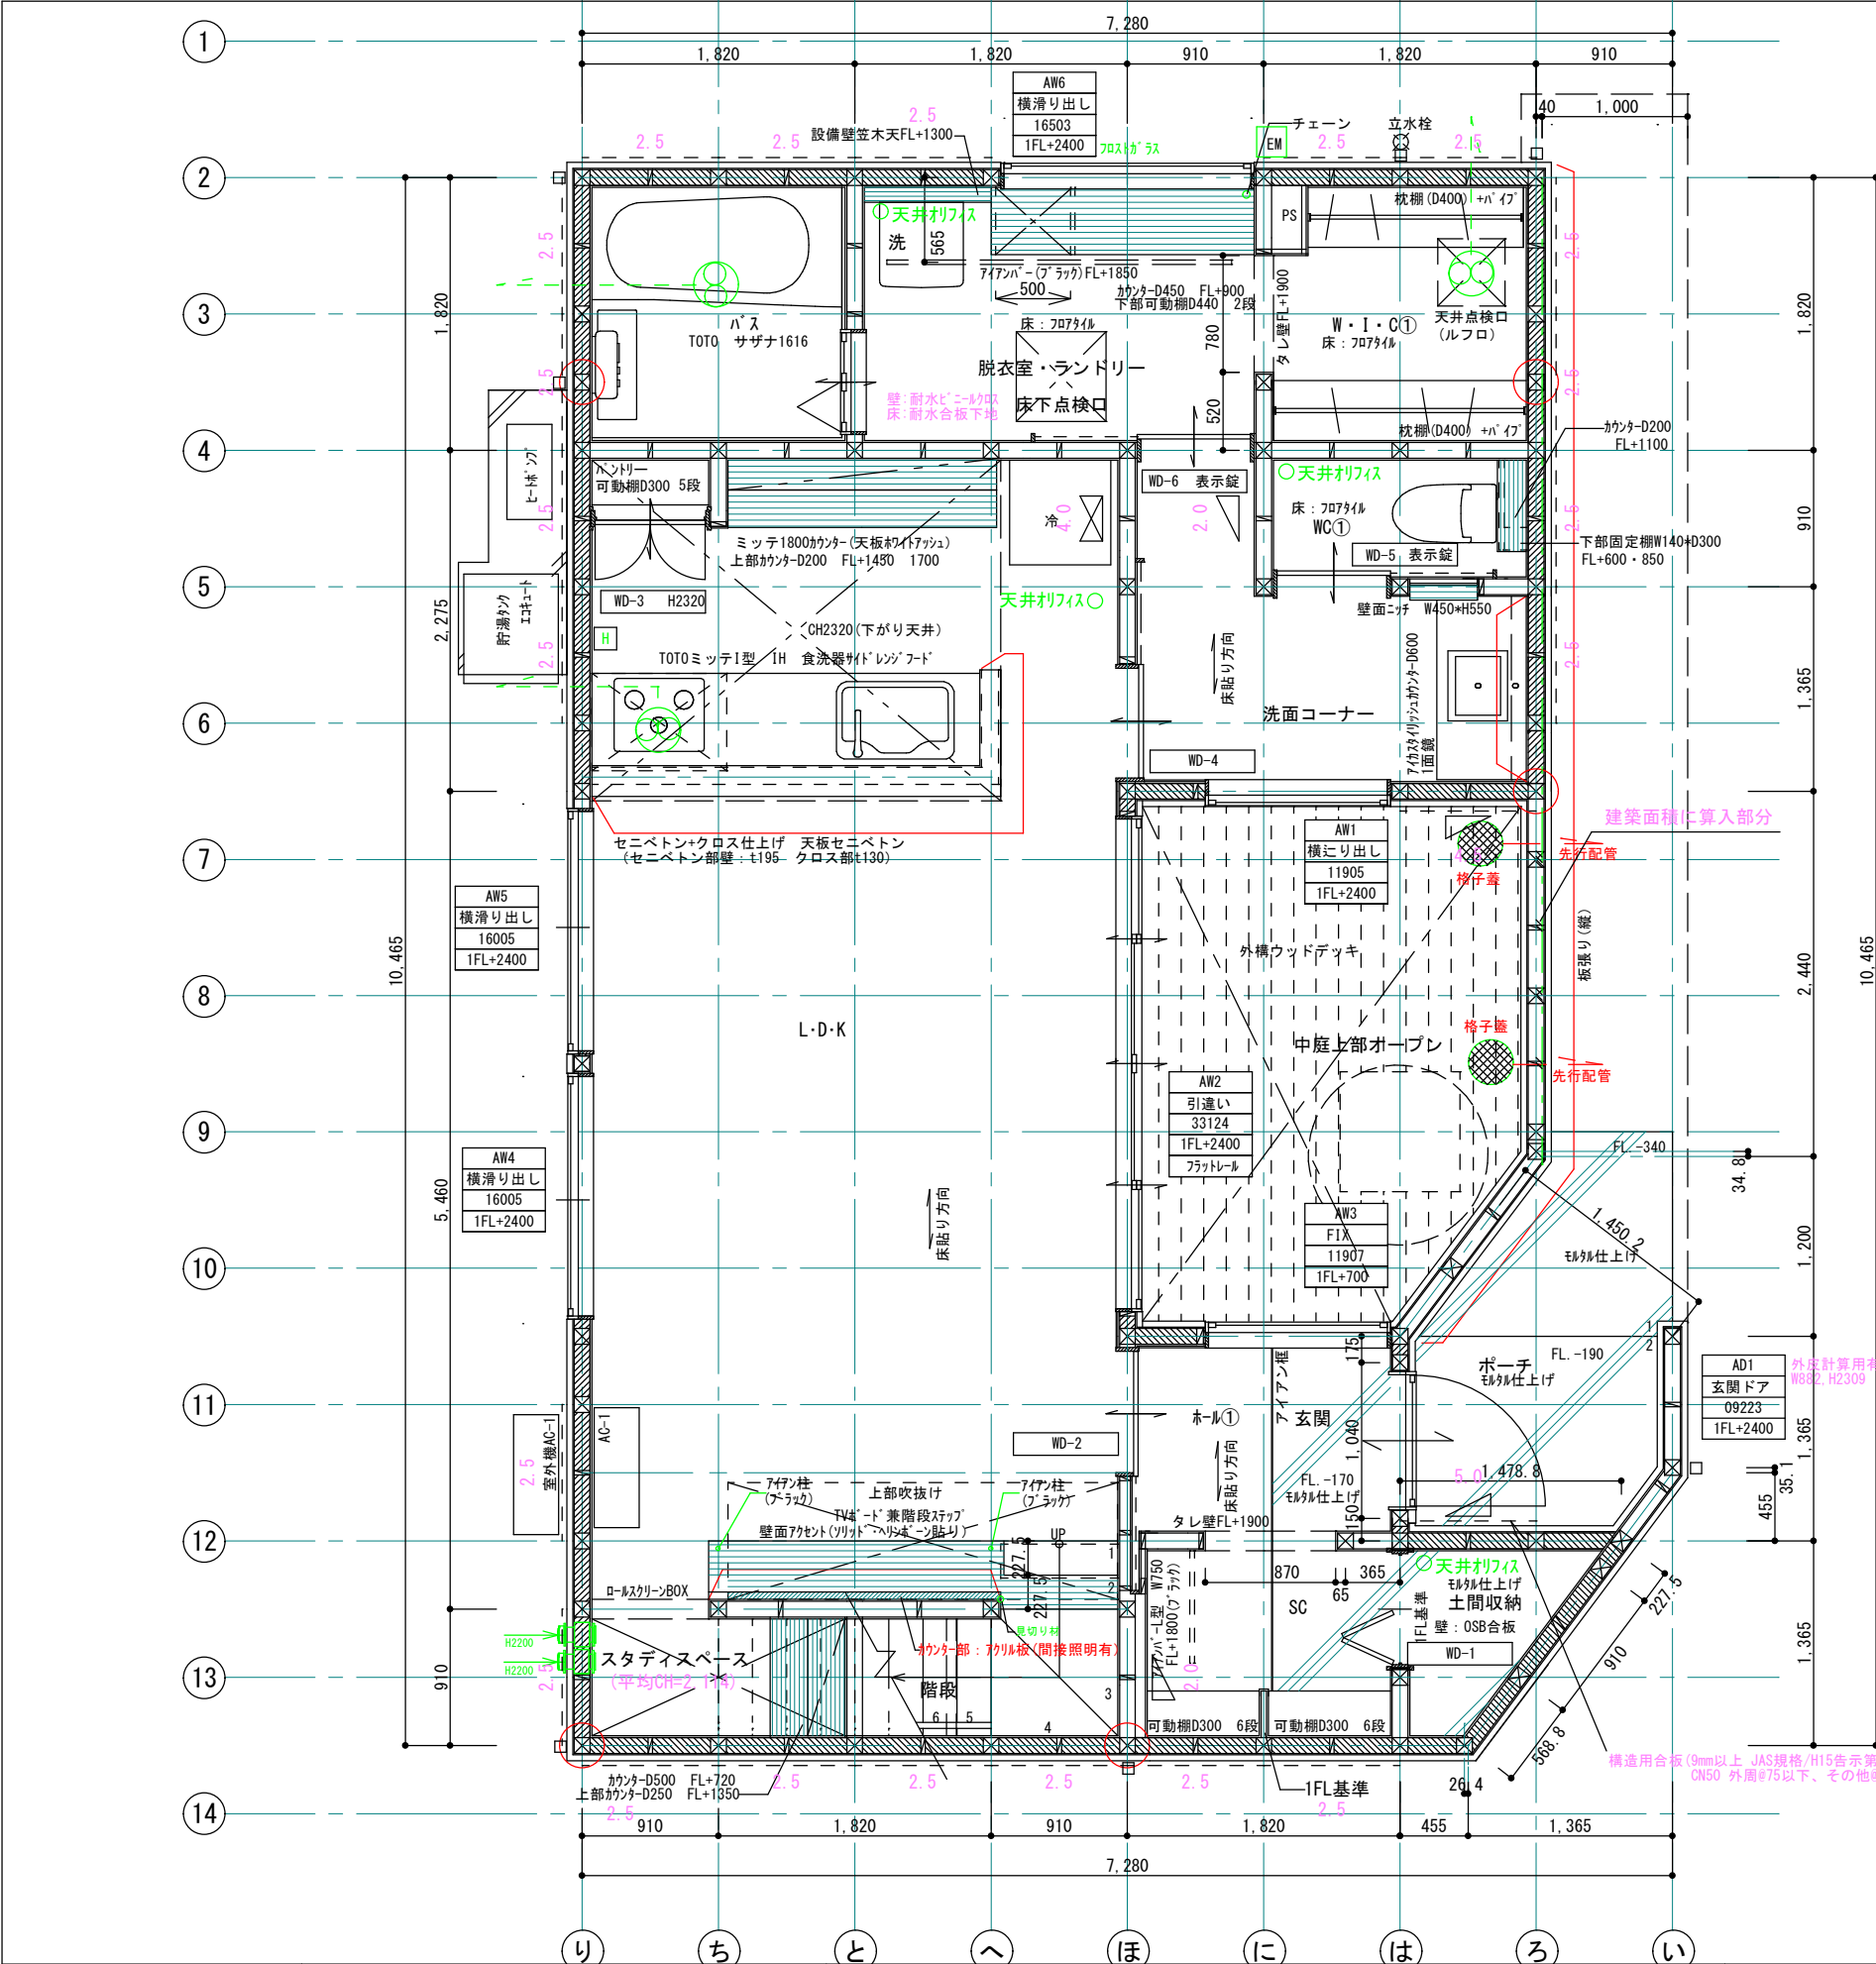

建築面積求積表			
番号	計算式	(m)	面積 (㎡)
A1	6.37*4.095		26.085150
A2	3.64*3.64		13.249600
A3	5.46*2.73		14.905800
A4	(1.82+0.455)*1.82*1/2		2.070250
A5	1.82*0.91		1.656200
A6	1.82*1.20*1/2		1.092000
A7	(6.535+6.58775)*0.04*1/2		0.262455
計算式 A1 + A2 + A3 + A4 + A5 + A6 + A7			59.321455
合計			59.32

建築面積求積図 S=1/200

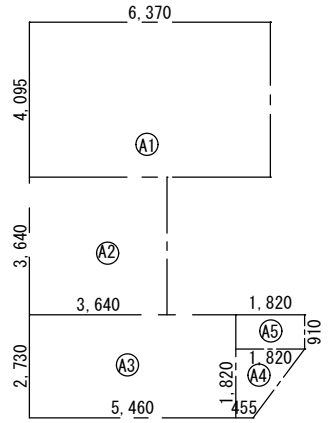

1階床面積図 S=1/200			
番号	計算式	(m)	面積 (㎡)
A1	6.370*4.095		26.085150
A2	3.640*3.640		13.249600
A3	5.460*2.730		14.905800
A4	(1.82+0.455)*1.82*1/2		2.070250
A5	1.82*0.91		1.656200
計算式 A1 + A2 + A3 + A4 + A5			57.967000
合計			57.96

1階床面積図 S=1/200

延床面積
 $57.96 + 38.61 = 96.57 \text{ m}^2$

※フラット7部小屋裏点検について
ダクトライトを利用し、パイプスコープ等にて検査を行う。

G2仕様

壁付け 住宅用火災報知器			数量
[H] 熱感知	熱感知器	電池式(単独型)	1
		露出型	
壁付け 住宅用火災報知器			数量
[S] 煙感知	煙感知器	電池式(単独型)	
		露出型	

※ 煙感知器は壁・梁より600mm以上離す
壁に取付ける場合 天井から150mm以上500mm以内離す
換気扇・エアコン吹出口から1500mm以上離す

* 凡例

⊗

通柱 (105×105)

⊗

管柱 (105×105)

△

片筋違い
(2.00倍 45×90)
(例 左:柱脚 右:柱頭)

△

たすき掛筋違い
(4.00倍 45×90)

構造用合板 (2.50倍)
(t=9 ダクト)

□

床点検口

□

天井点検口

⊗

換気扇

→

給気口