


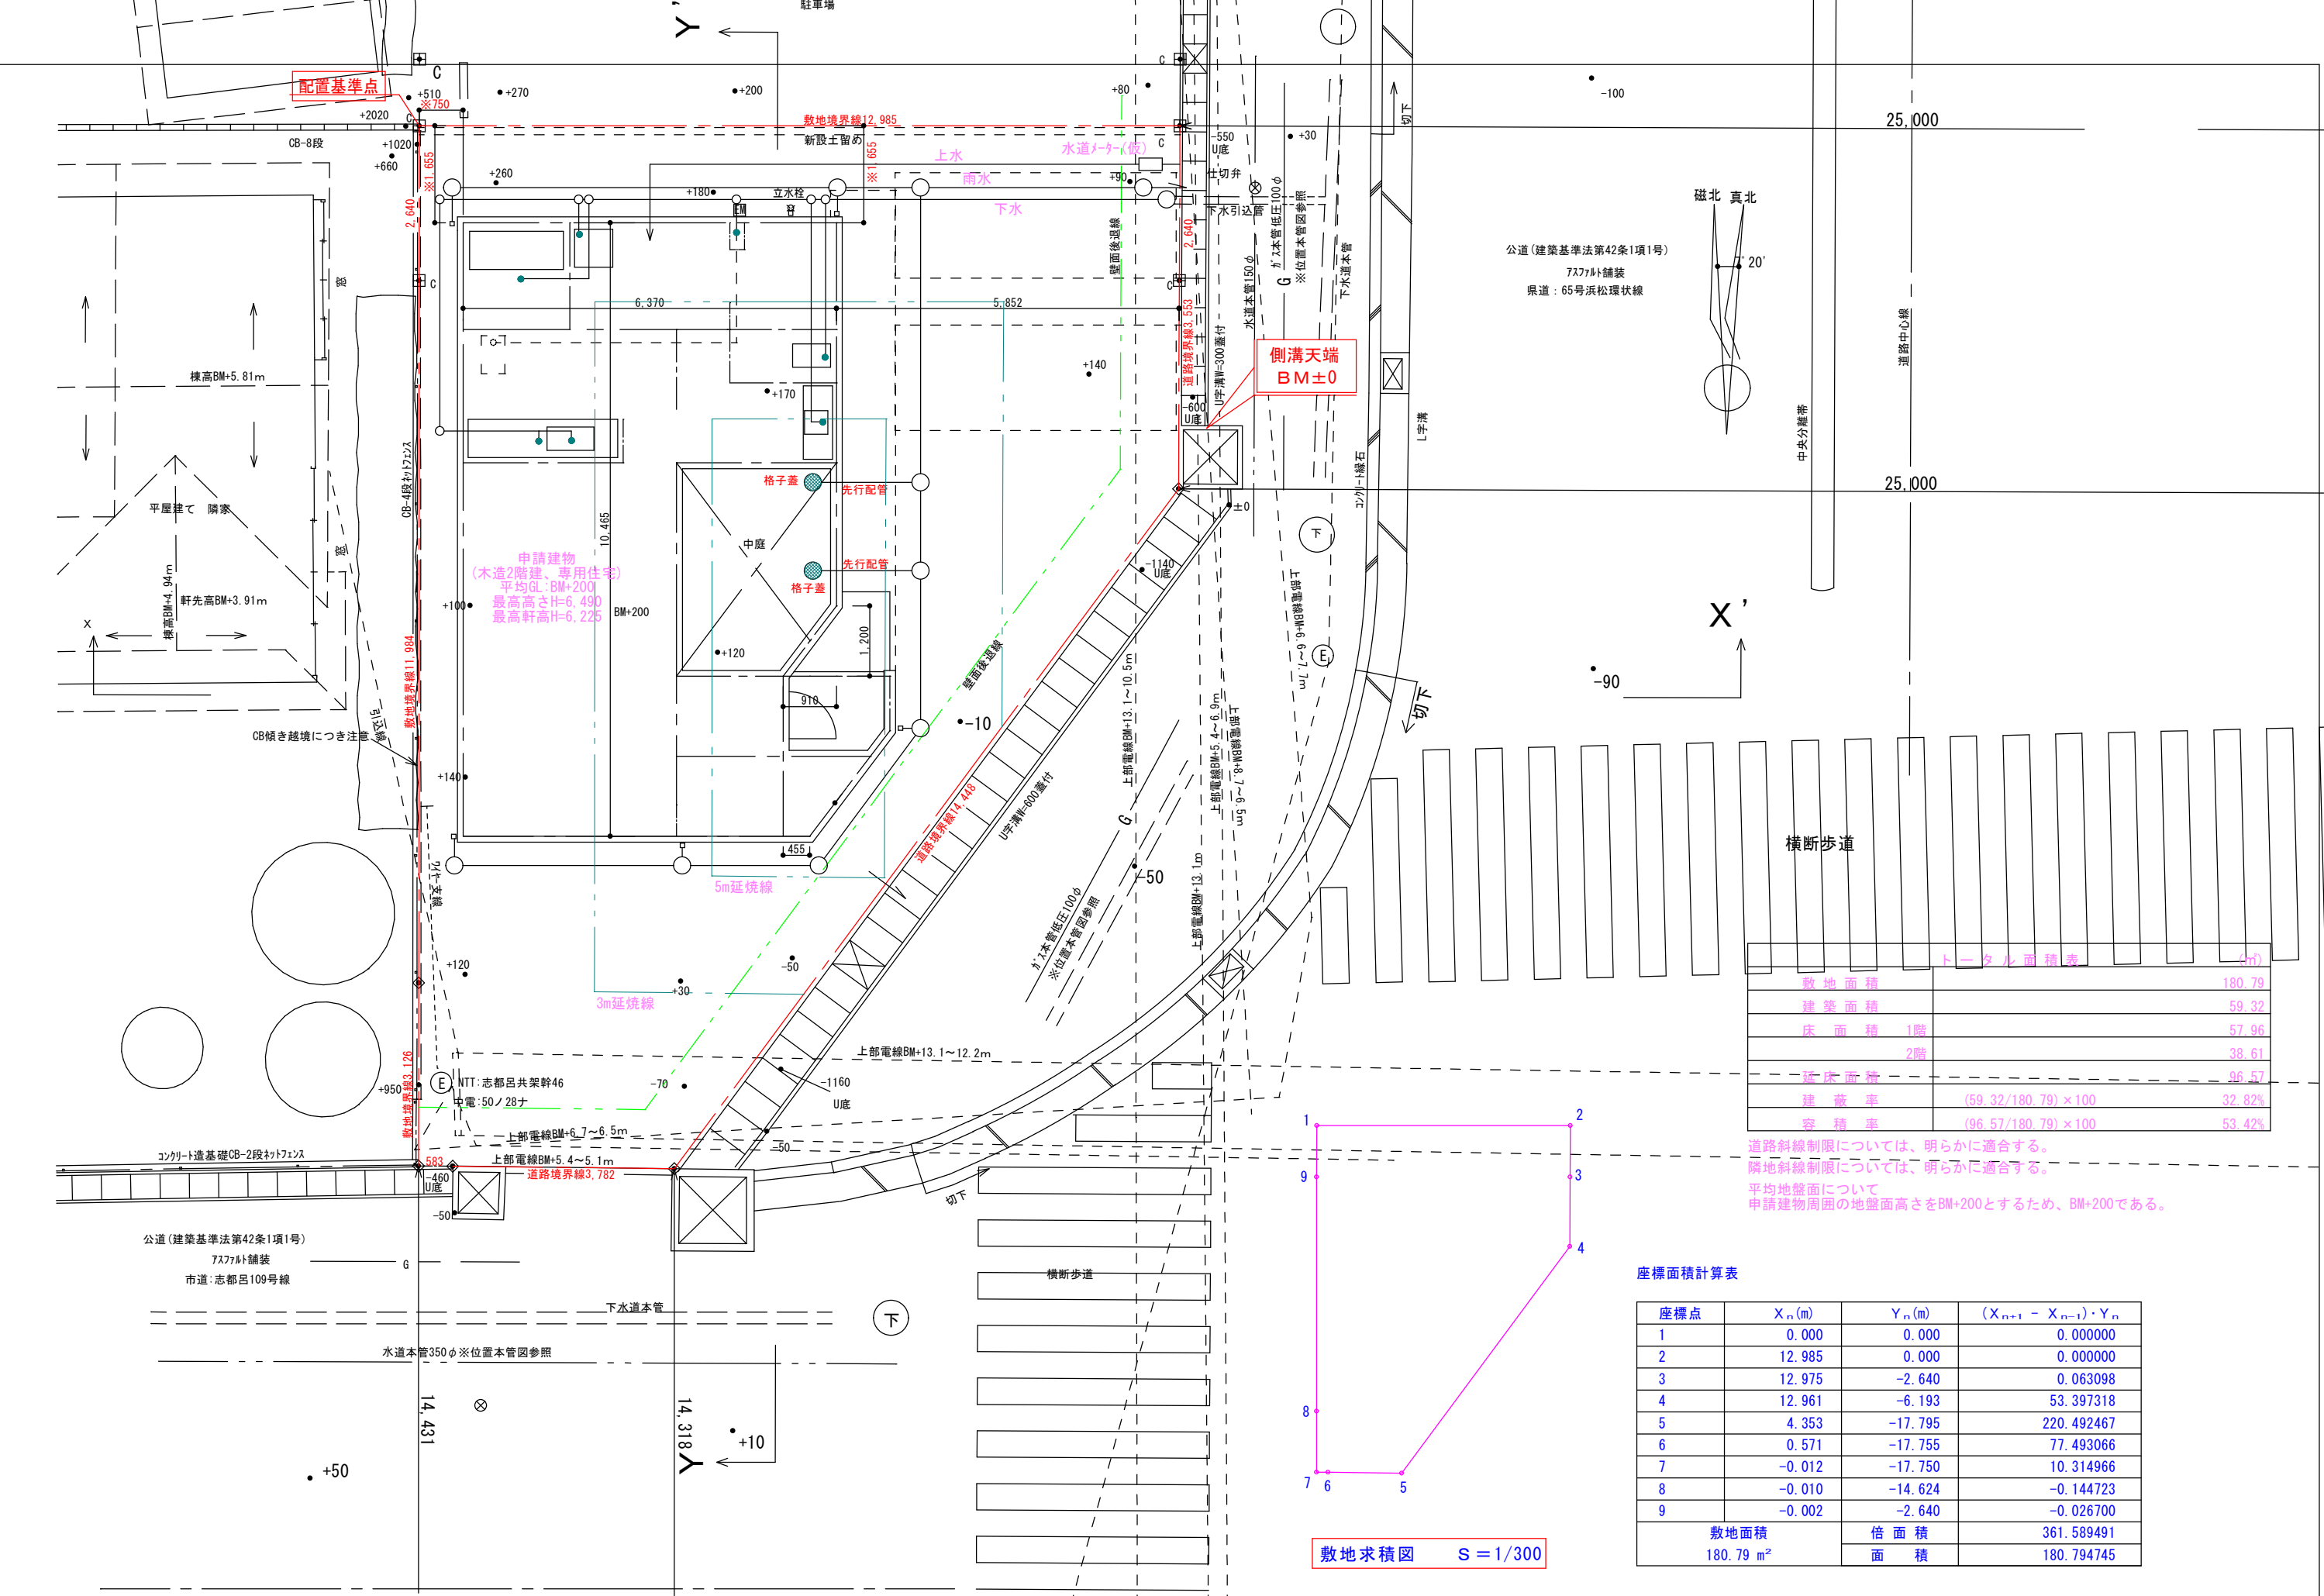

トータル面積表 (㎡)	
敷地面積	180.79
建築面積	59.32
床面積 1階	57.96
2階	38.61
延床面積	96.57
建築率	(59.32/180.79) × 100
容積率	(96.57/180.79) × 100

道路斜線制限については、明らかに適合する。
隣地斜線制限については、明らかに適合する。
平均地盤面について
申請建物周囲の地盤面高さをBM+200とするため、BM+200である。

敷地求積図 S = 1/300

座標面積計算表

座標点	X _n (m)	Y _n (m)	(X _{n+1} - X _{n-1})・Y _n
1	0.000	0.000	0.000000
2	12.985	0.000	0.000000
3	12.975	-2.640	0.063098
4	12.961	-6.193	53.397318
5	4.353	-17.795	220.492467
6	0.571	-17.755	77.493066
7	-0.012	-17.750	10.314966
8	-0.010	-14.624	-0.144723
9	-0.002	-2.640	-0.026700
敷地面積 180.79 m ²		倍面積 面積	361.589491 180.794745